

ENERAL NOTES :-



HIS DRAWING IS THE PROPERTY OF
design & ARchitecture bureau (DAR)
.O.BOX 31122 DUBAI U.A.E TEL 2828800 FAX 2828877

IT IS NOT ALLOWED TO REPRODUCE IT'S CONTENTS IN ANY
ORM EXCEPT FOR THE PURPOSE FOR WHICH IT IS INTENDED.

HIS DRAWING IS NOT TO BE SCALED,
TATED DIMENSIONS ONLY ARE TO BE CONSIDERED.

NY DISCREPANCIES ARE TO BE BROUGHT TO THE
TTENTION OF THE ENGINEER AND RESOLVED
EFORE COMMENCEMENT OF ANY WORK.

BEACH VIEW

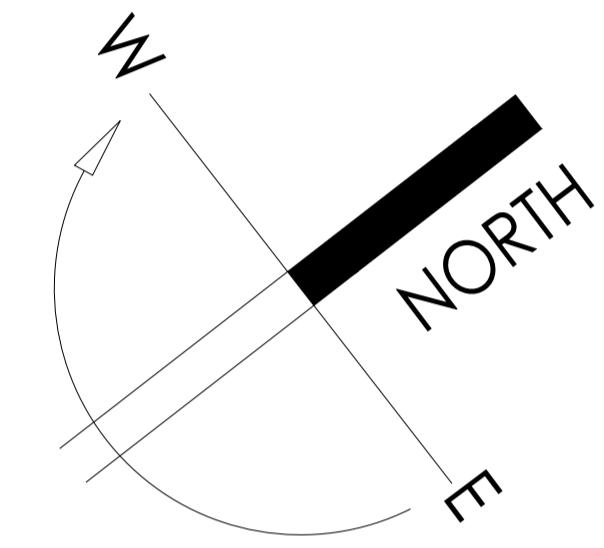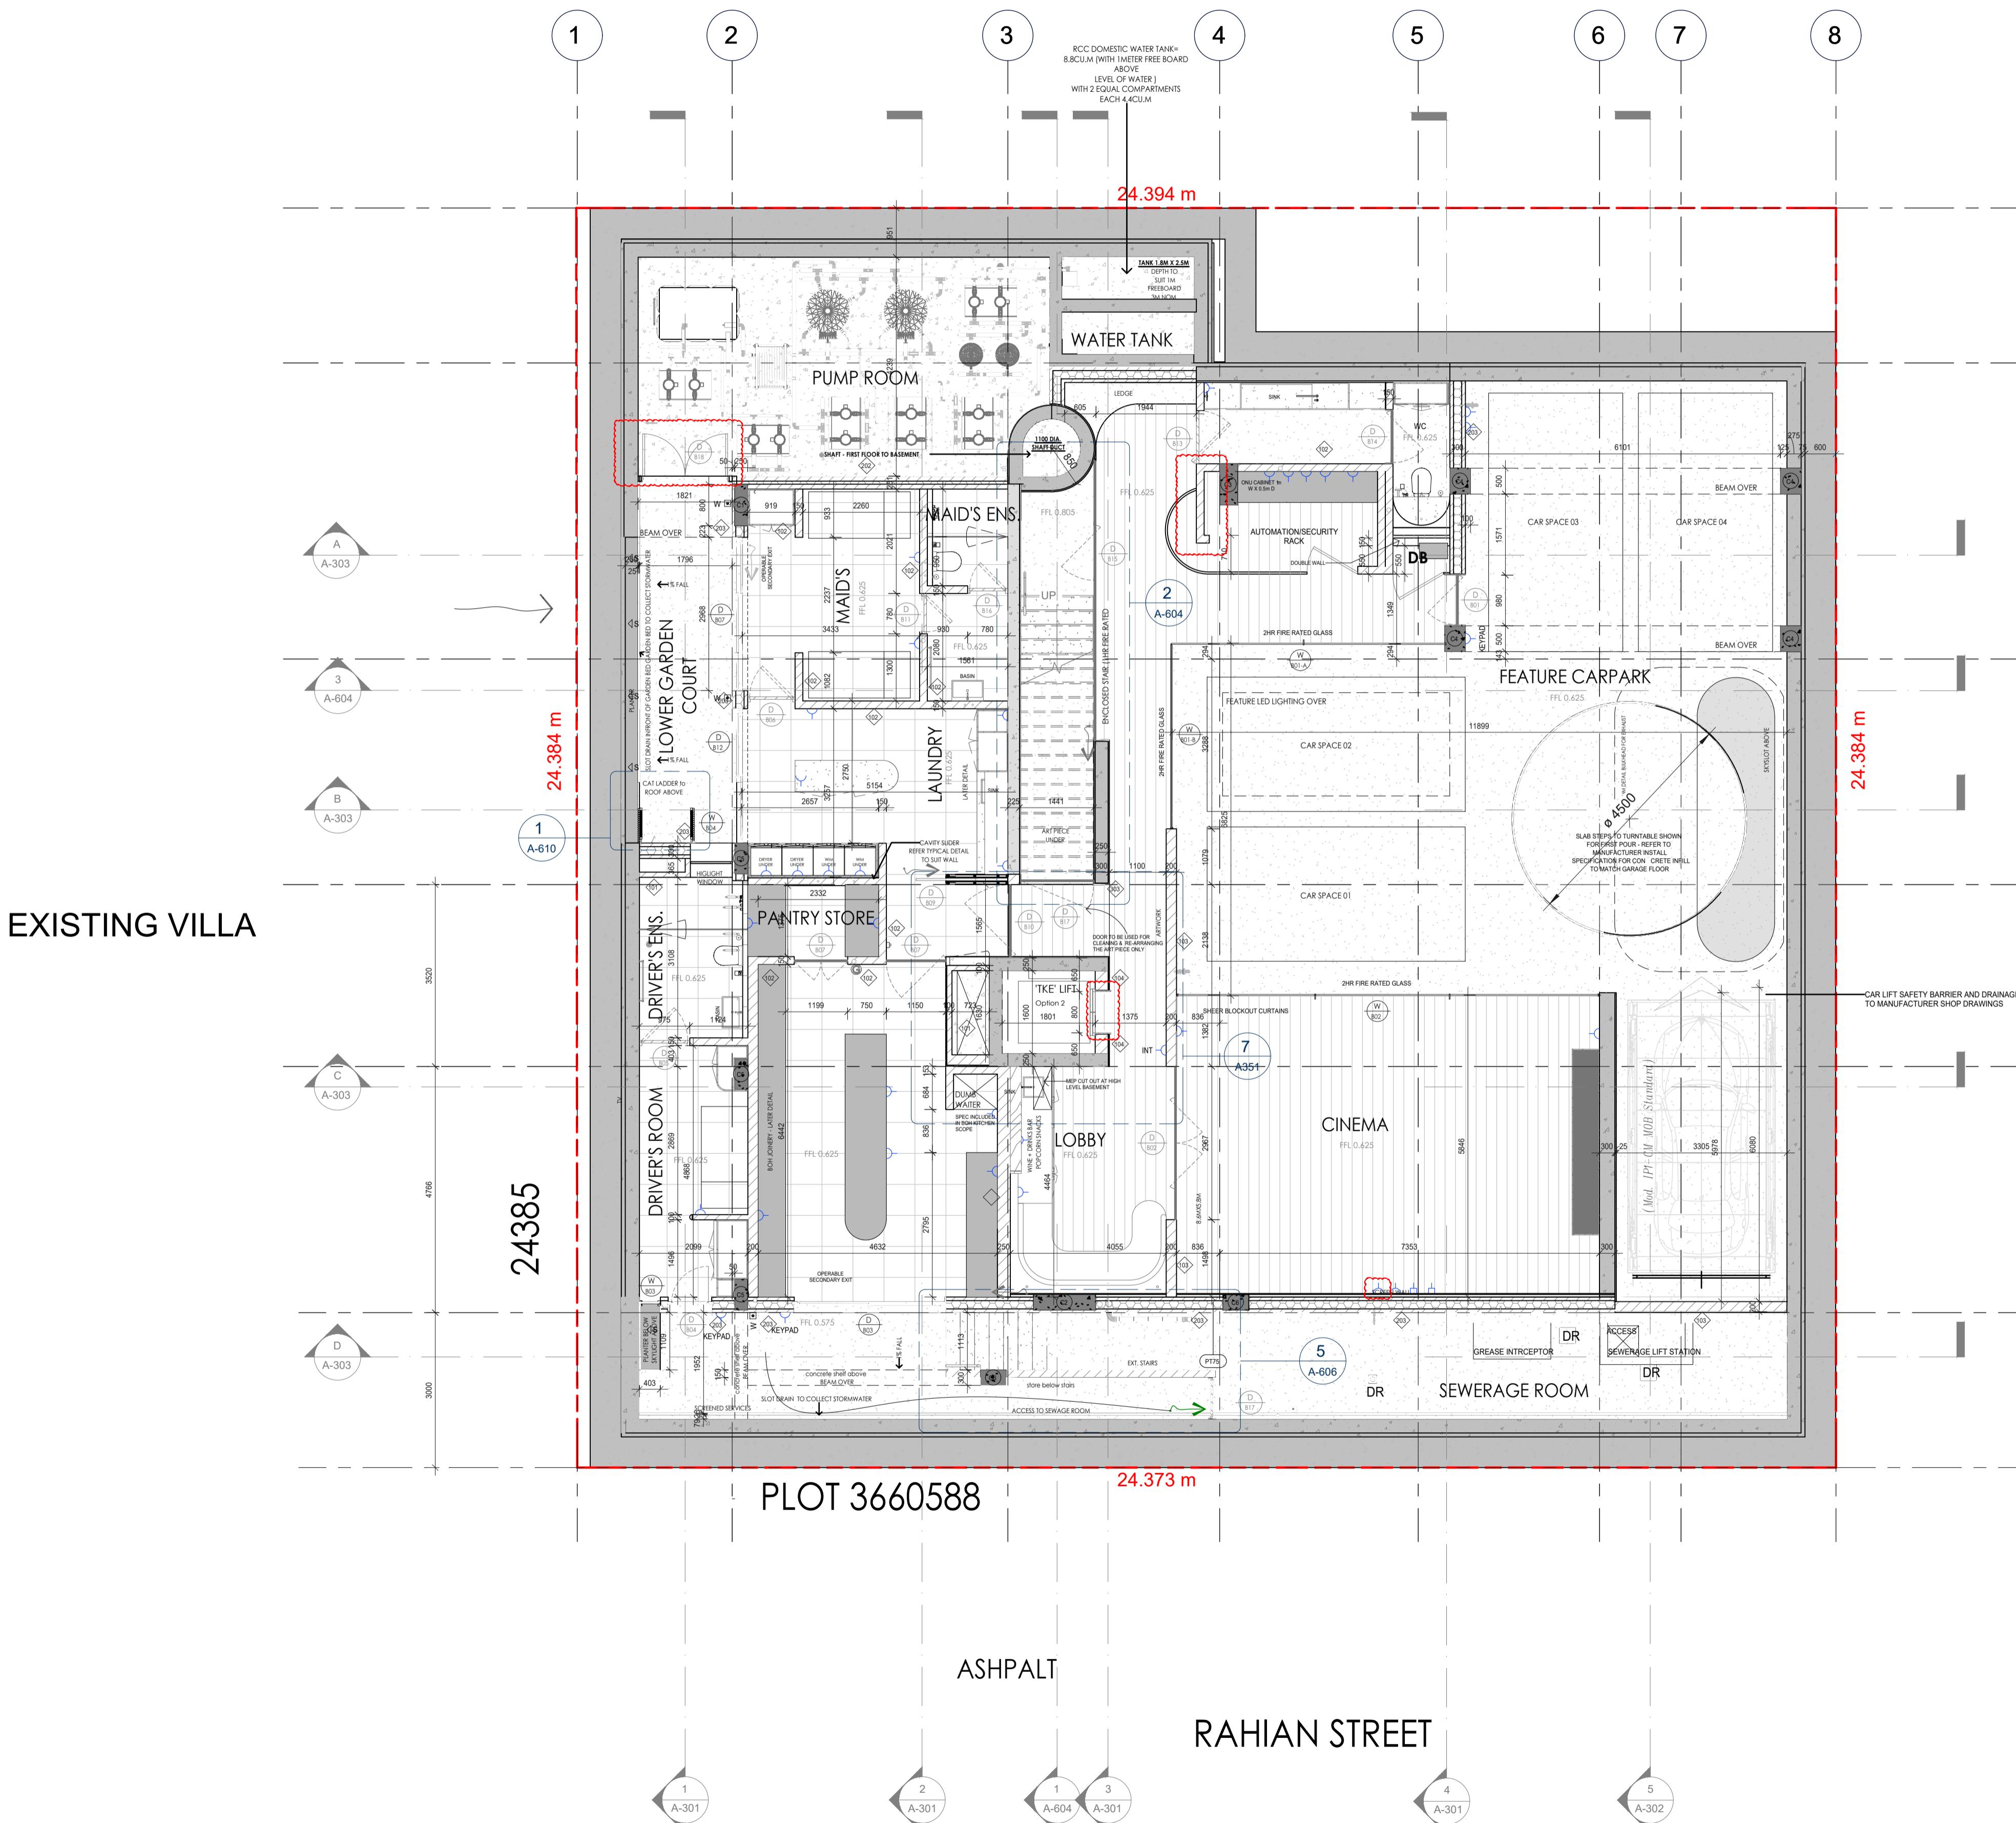

ISSUED FOR TENDER

 Design & ARchitecture bureau | DAR
Consulting Architects & Engineers

	18.02.2025	ISSUED FOR TENDER	-
	24.01.2025	ISSUED FOR TENDER	-
	20.12.2024	ISSUED FOR TENDER	-
	Date.	Description.	Rev. By

KISTING VILLA

REVISIONS AND ISSUES

ALTA

Job Title
**PROPOSED 1B+G+F+1ST
ROOF+2ND ROOF FLOORS
RESIDENTIAL VILLA
ON PLOT No. 3660588,
JMM SUQEIM THIRD, DUBAI, UAE.**

Lead Consultant



Design & ARchitecture bureau | DAR
Competence Architecture & Engineering

Design: Anubhav

mckimm

Project No. DB - 24 - 801

Drawing Title

BASEMENT LEVEL PLAN

Scale @ A1 Drawn Checked Date

1:75 TJ JULY 2024

North	Drawing No.	Rev. No.
	A-100	T2